




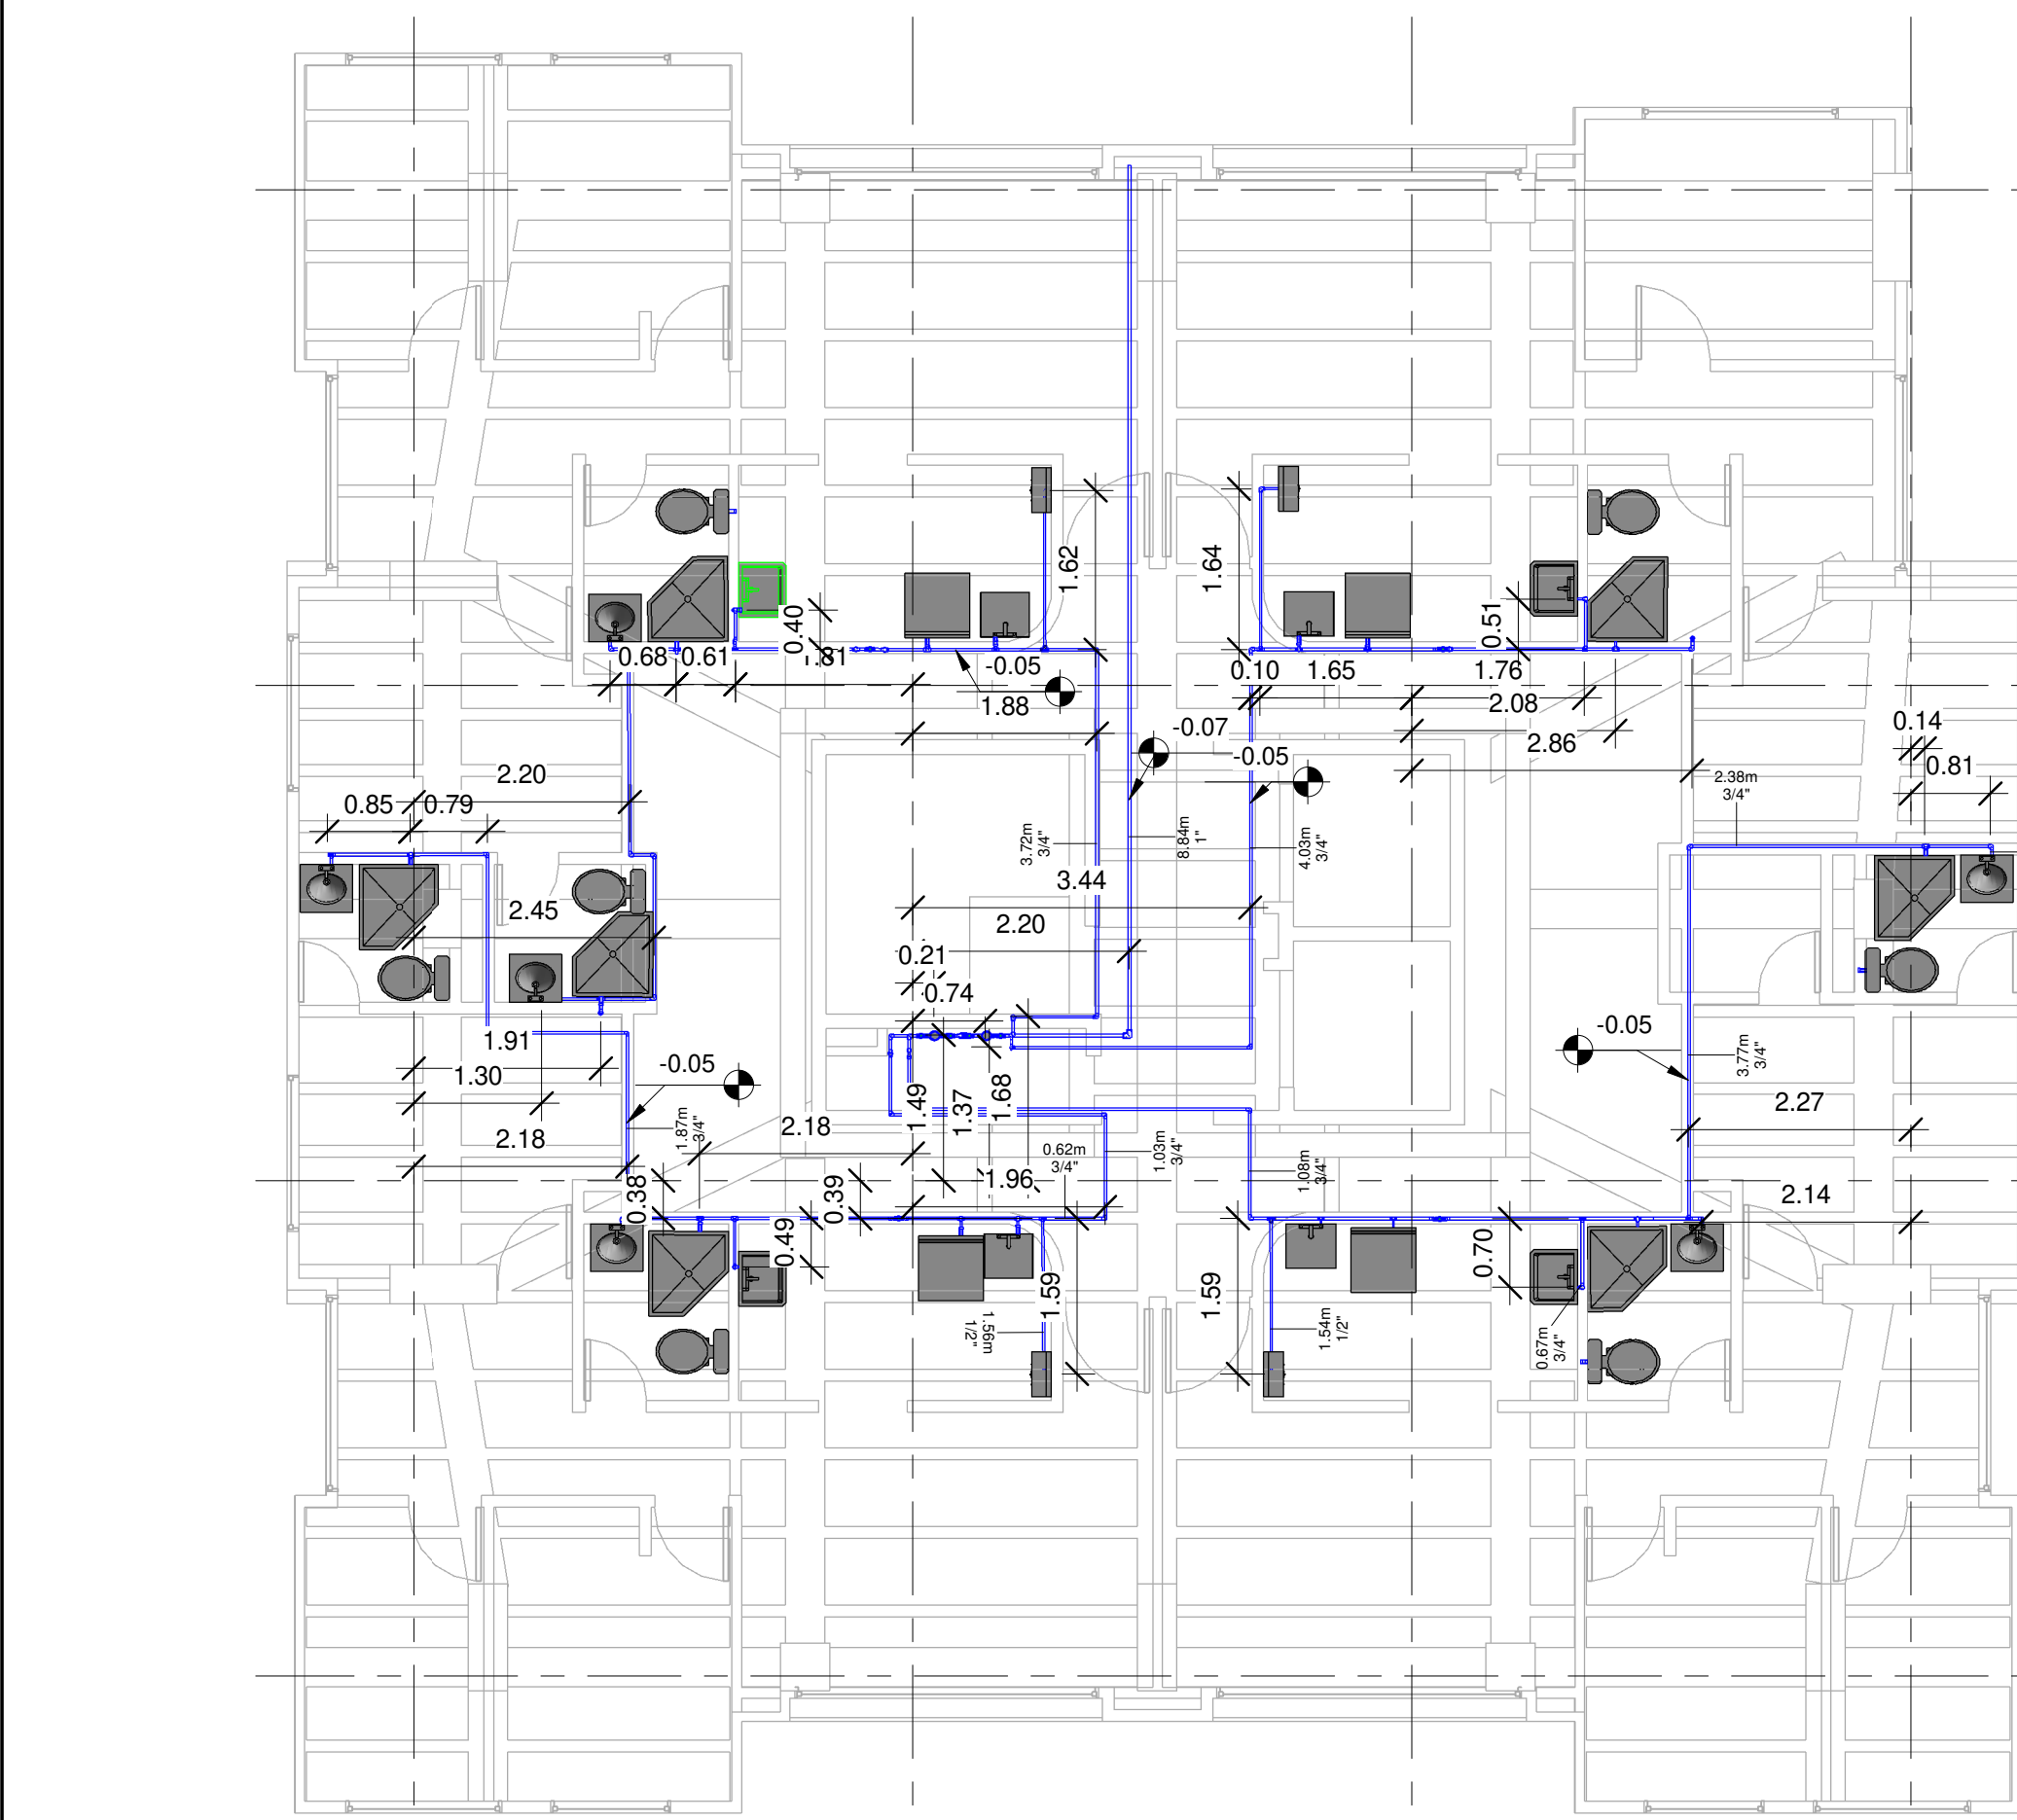


A Instalacion domestica fria
1 : 75

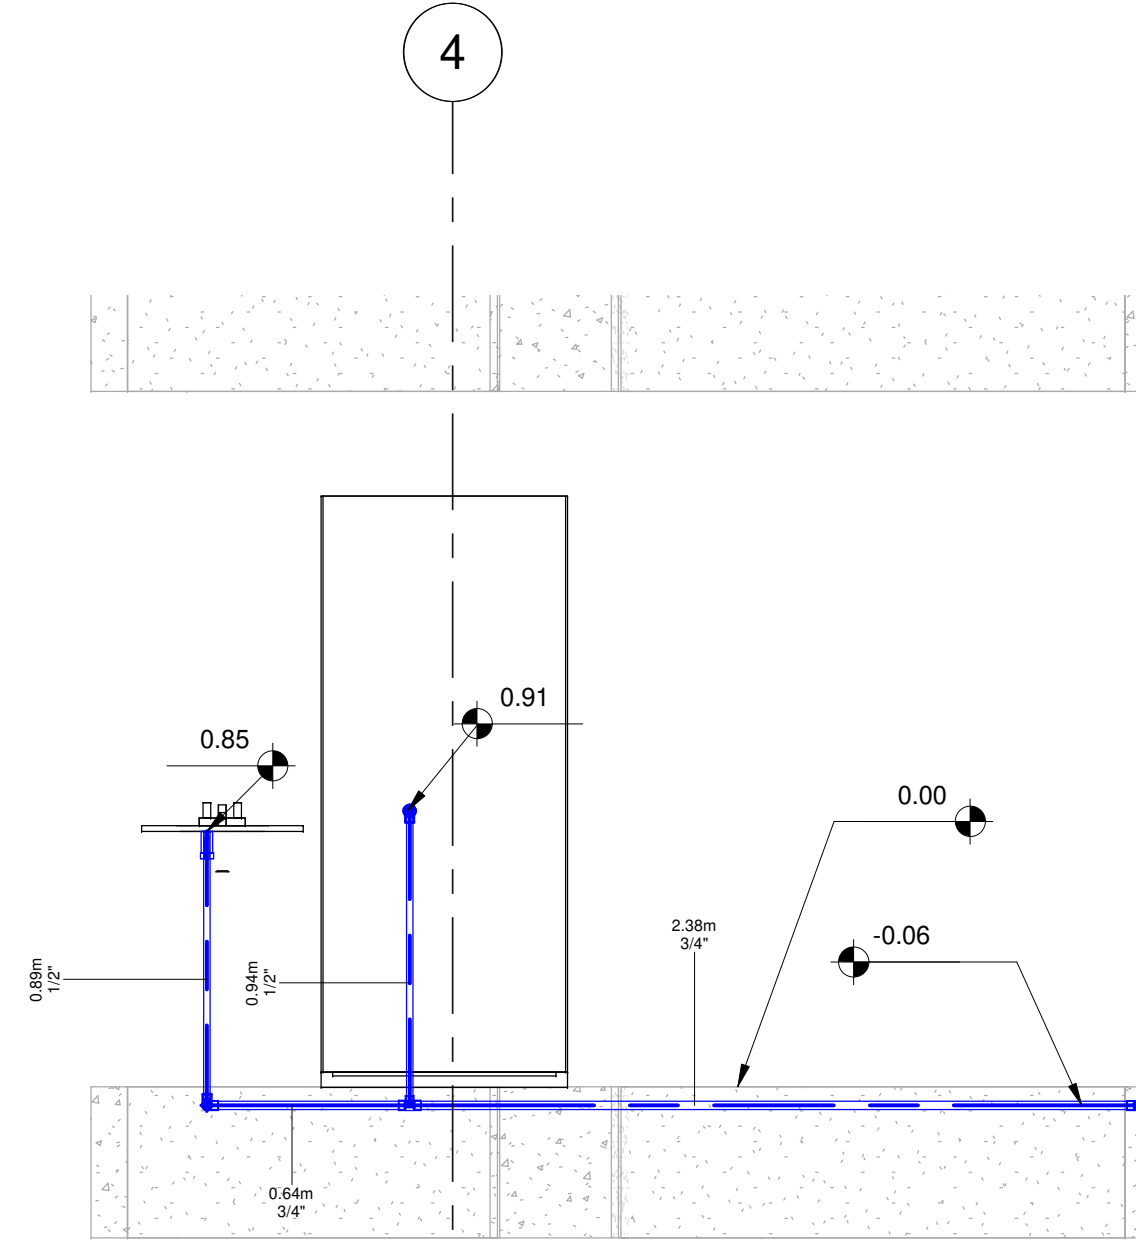


3 Red agua fria aparato critico
1 : 25

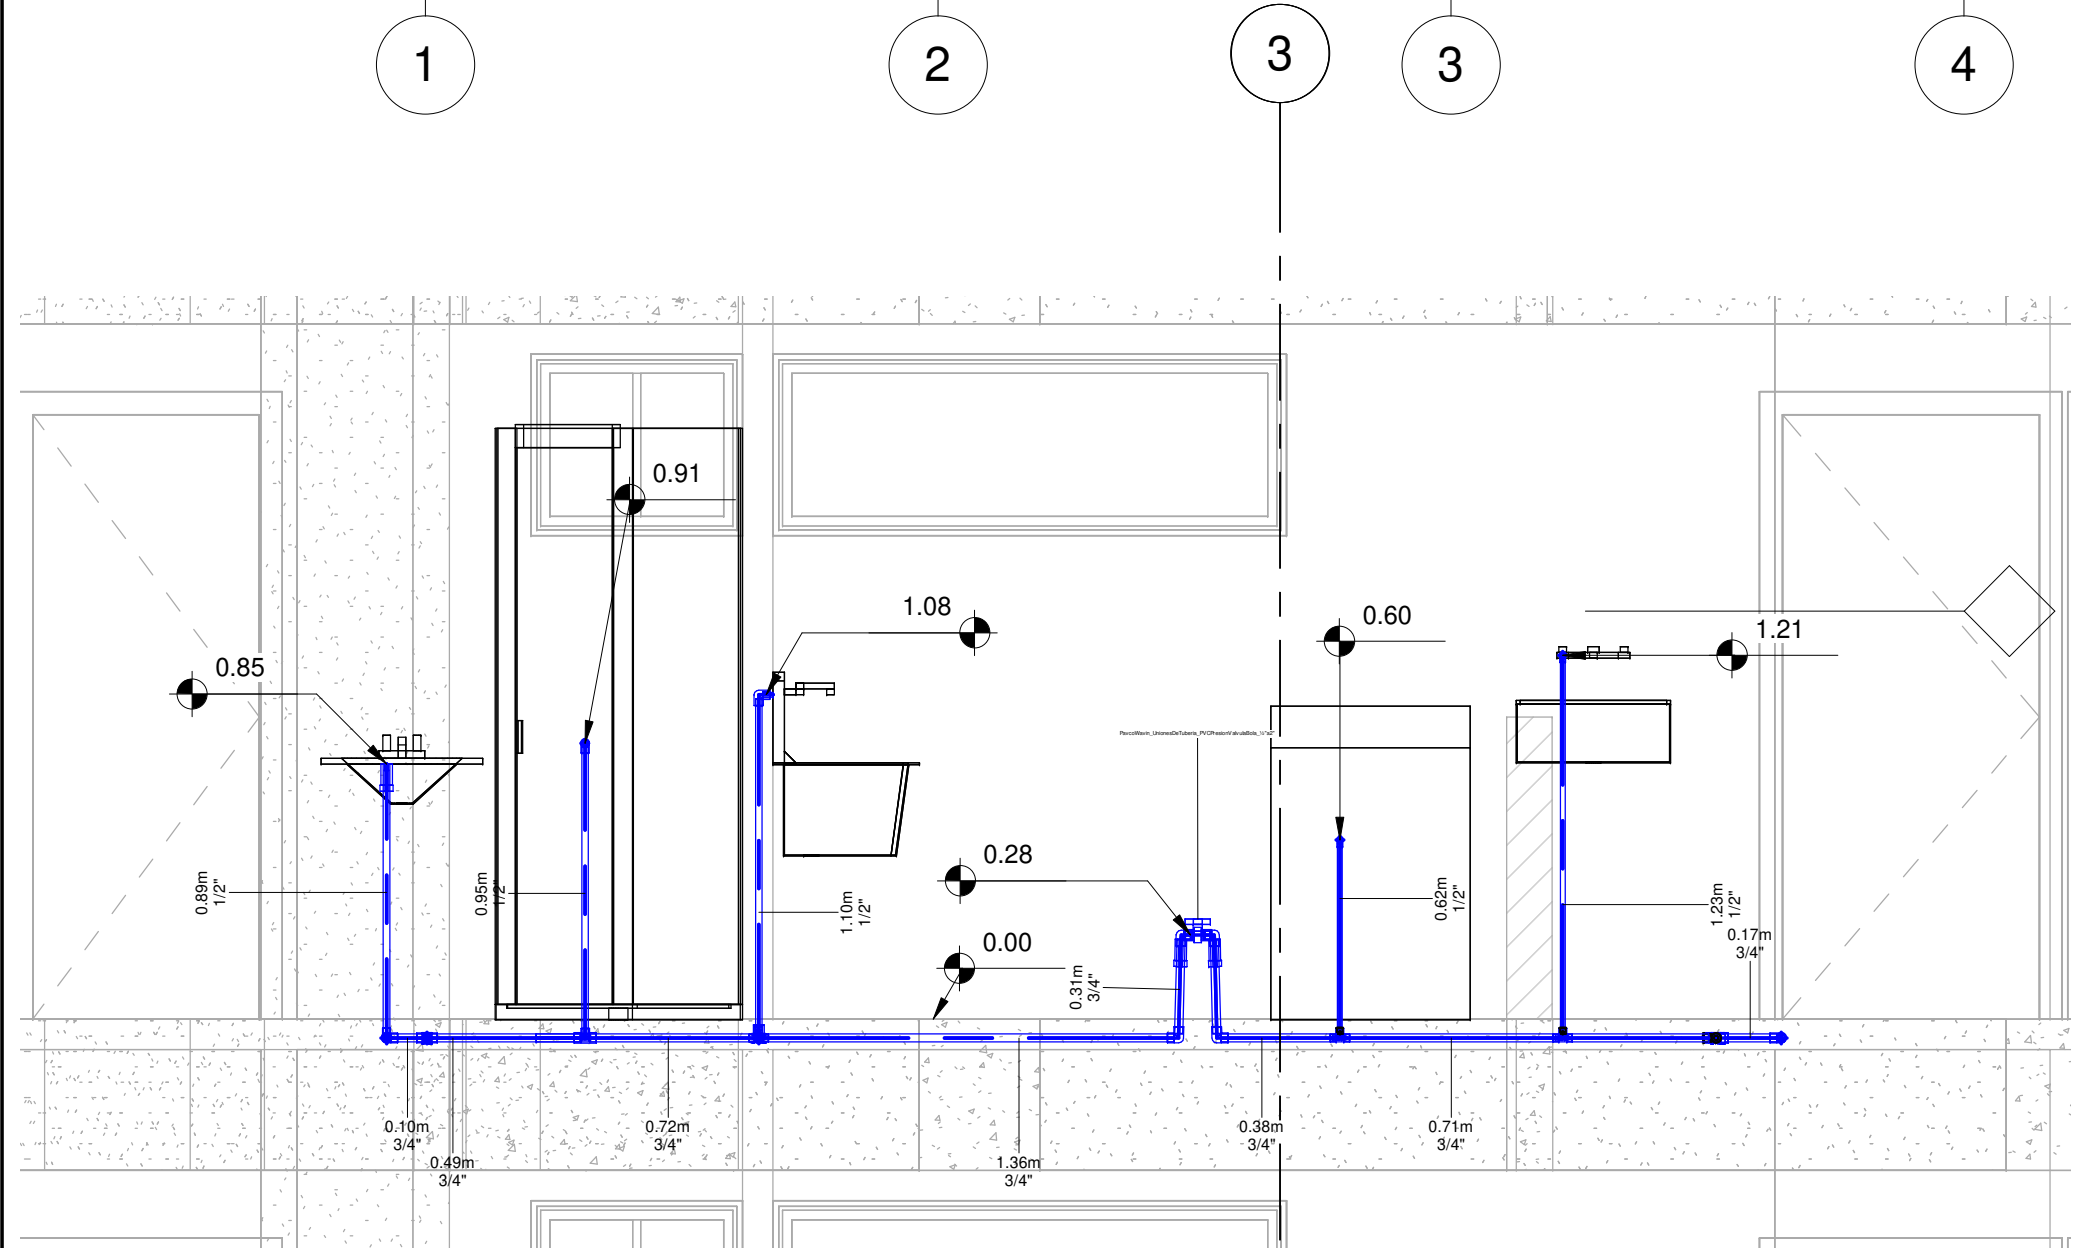

2 Distribucion red agua fria
1 : 25

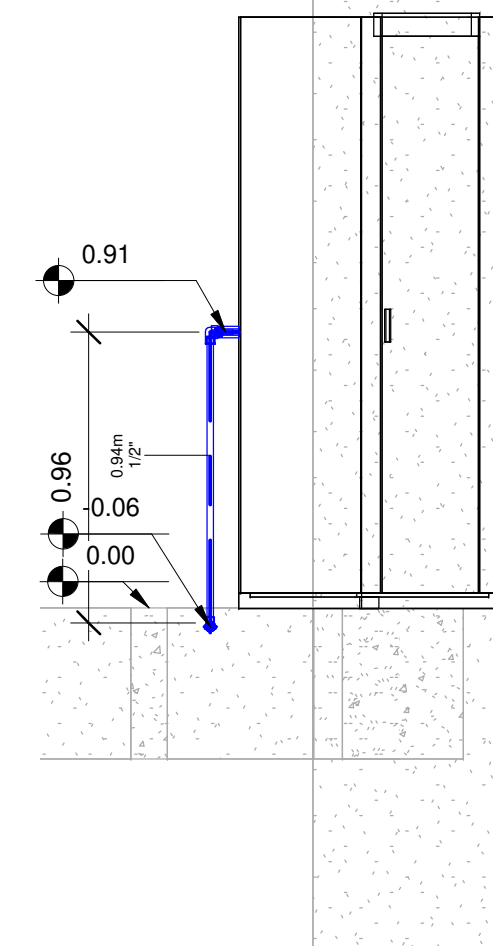

1 Aparato critico
1 : 25

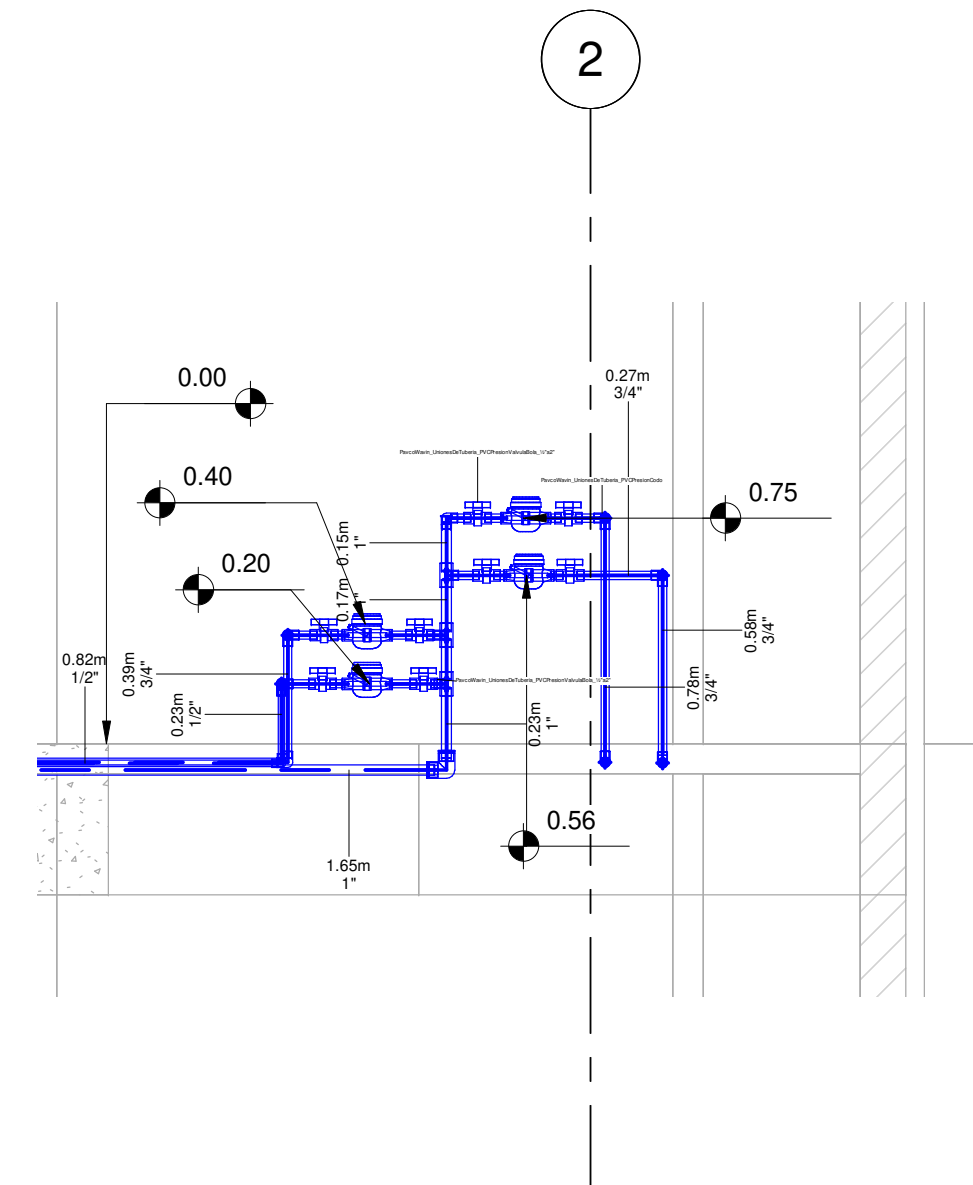

4 Medidores
1 : 25

Propietario	
	
NIT propietario	
860.013.720	
Nombre del proyecto	
Conjunto torres Asturias Real	
Dirección del proyecto	
Avenida Carrera 14 (Caracas) No. 37 – 48 sur	
Cuidad del proyecto	
Bogota D.C	
Nombre del plano	
Plano de redes de agua fria	
material tuberías	
Se muestra en el plano H-01, plano de especificaciones	
Contenido	
Escala	Version
As indicated	1.
Normatividad	
Especificaciones	
Especialidad	
Representante legal	
Hidrotecnia	David Sebastian Becerra
Encargados proyecto	

Archivo	
Total planos: 1	Fecha: 16/10/2020 6:21:51 p. m.
Número plano: H-02	Dibujante: David Becerra
Empresa de diseño	
